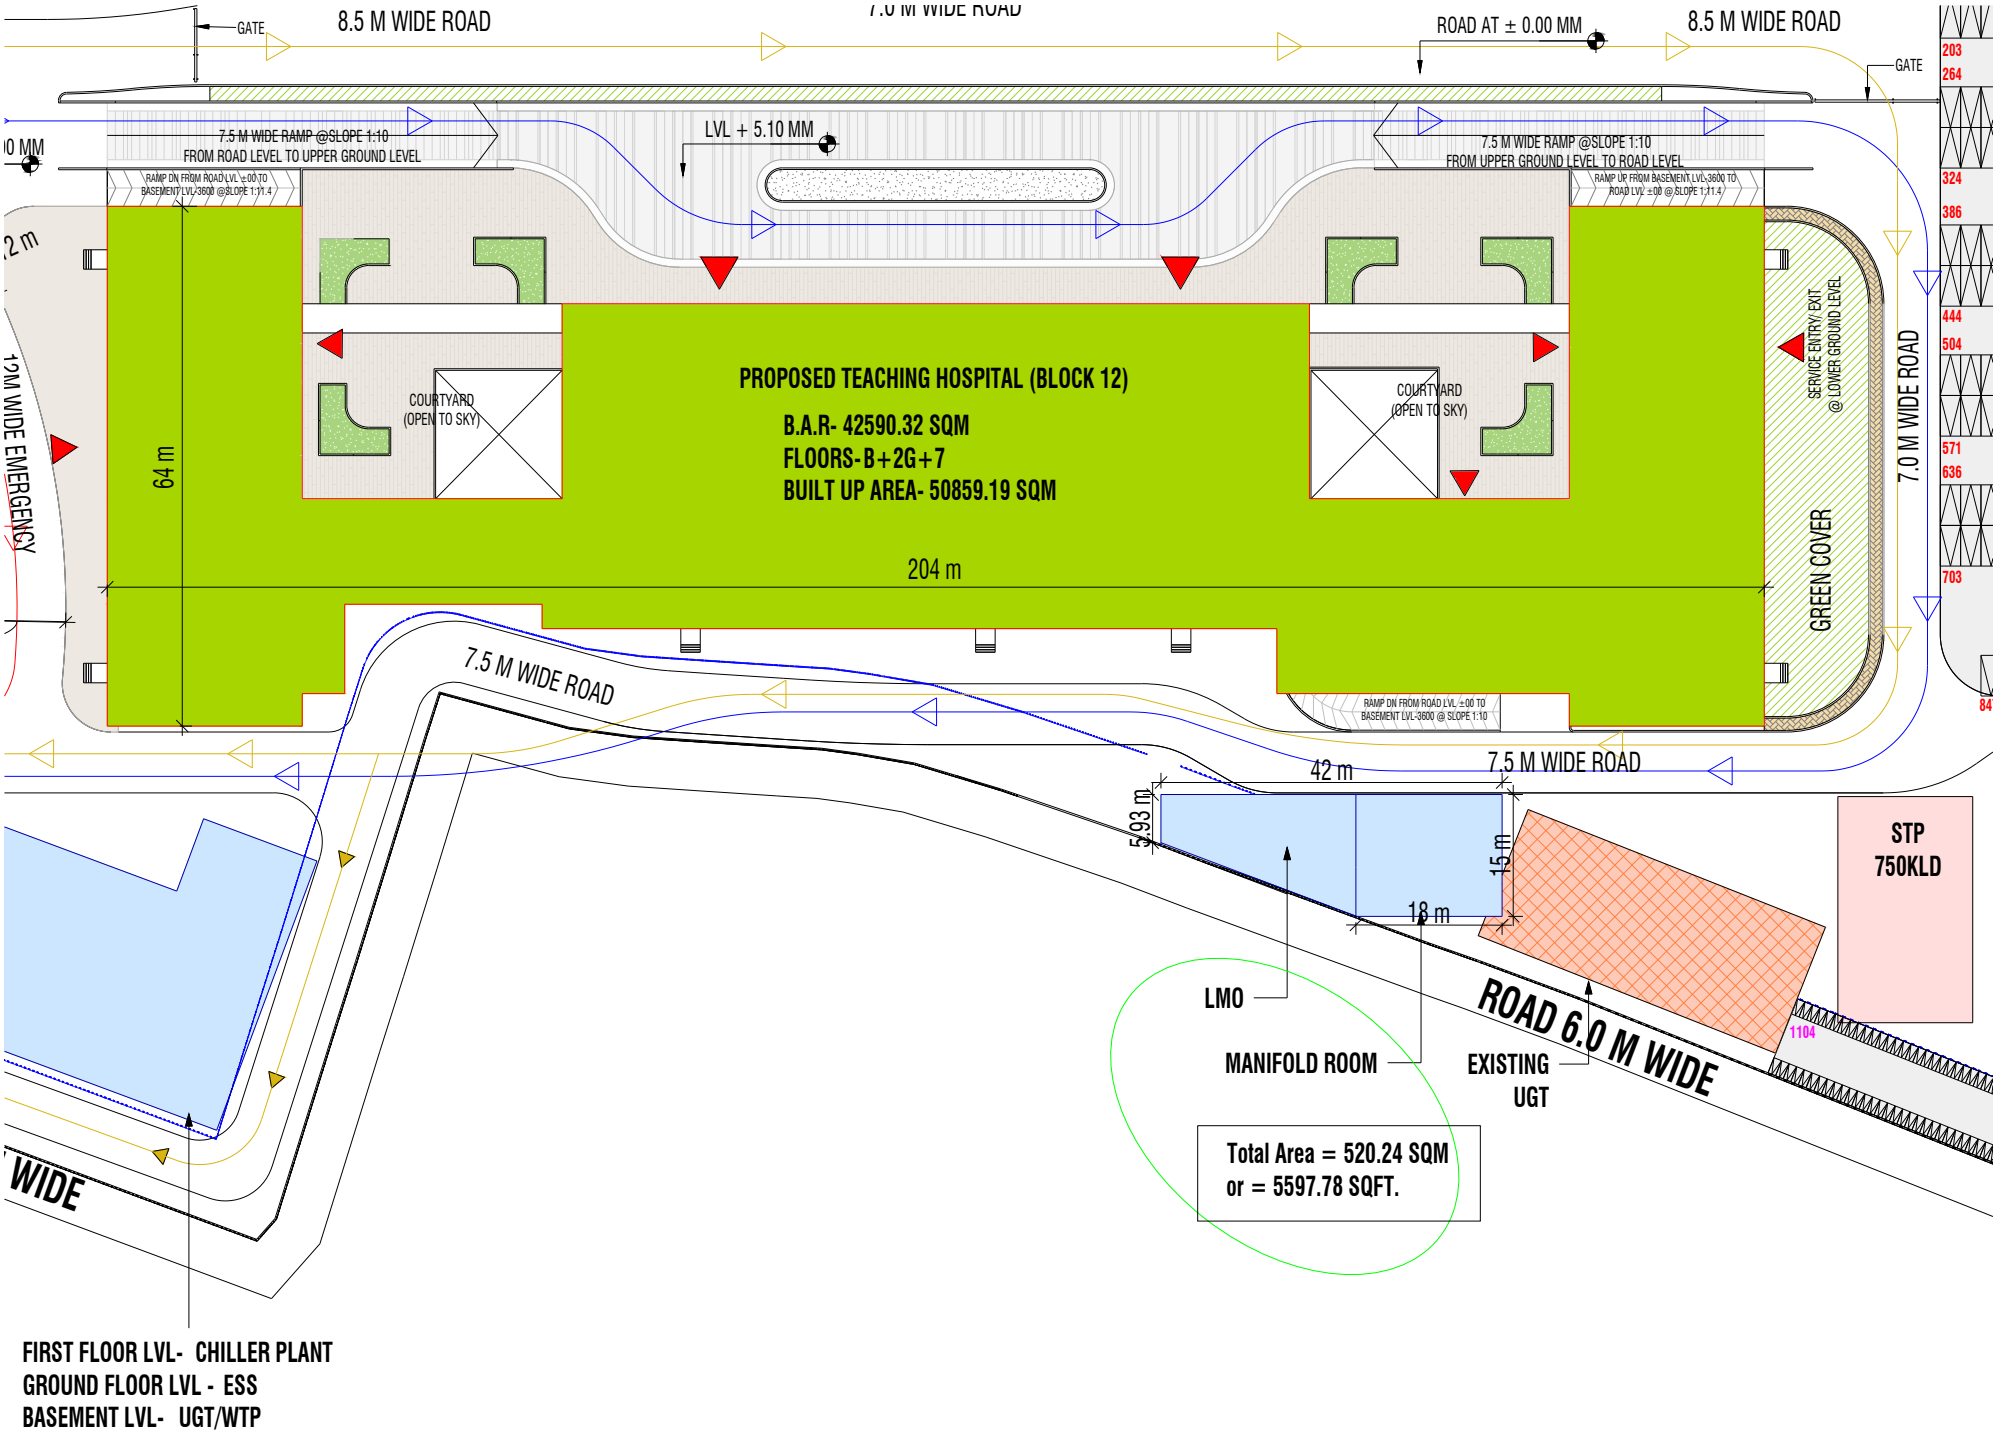

GATE
8.5 M WIDE ROAD
ROAD AT ± 0.00 MM
8.5 M WIDE ROAD
GATE
7.5 M WIDE RAMP @SLOPE 1:10
FROM ROAD LEVEL TO UPPER GROUND LEVEL
LVL + 5.10 MM
7.5 M WIDE RAMP @SLOPE 1:10
FROM UPPER GROUND LEVEL TO ROAD LEVEL
RAMP DN FROM ROAD LVL ±00 TO BASEMENT LVL-3600 @SLOPE 1:11.4
RAMP UP FROM BASEMENT LVL-3600 TO ROAD LVL ±00 @SLOPE 1:11.4
12M WIDE EMERGENCY
64 m
COURTYARD (OPEN TO SKY)
PROPOSED TEACHING HOSPITAL (BLOCK 12)
B.A.R- 42590.32 SQM
FLOORS-B+2G+7
BUILT UP AREA- 50859.19 SQM
COURTYARD (OPEN TO SKY)
SERVICE ENTRY/ EXIT @ LOWER GROUND LEVEL
7.0 M WIDE ROAD
GREEN COVER
204 m
RAMP DN FROM ROAD LVL ±00 TO BASEMENT LVL-3600 @ SLOPE 1:10
7.5 M WIDE ROAD
42 m
7.5 M WIDE ROAD
5.93 m
15 m
18 m
STP
750KLD
LMO
MANIFOLD ROOM
EXISTING UGT
ROAD 6.0 M WIDE
Total Area = 520.24 SQM
or = 5597.78 SQFT.
WIDE
FIRST FLOOR LVL- CHILLER PLANT
GROUND FLOOR LVL - ESS
BASEMENT LVL- UGT/WTP